DISTRICT : THE NILGIRIS

TALUK : KOTAGIRI

VILLAGE : JACKNARRAI

S.F.No : 23/1A1A & 4B

AREA AS PER PATTA :

S.F.No : 23/ 1A1A : 102969 Sqmt (25.44½ Acre)

S.F.No : 23/ 4B : 6300 Sqmt (1.55½ Acre)

TOTAL : 109269 Sqmt (27.00 Acre)

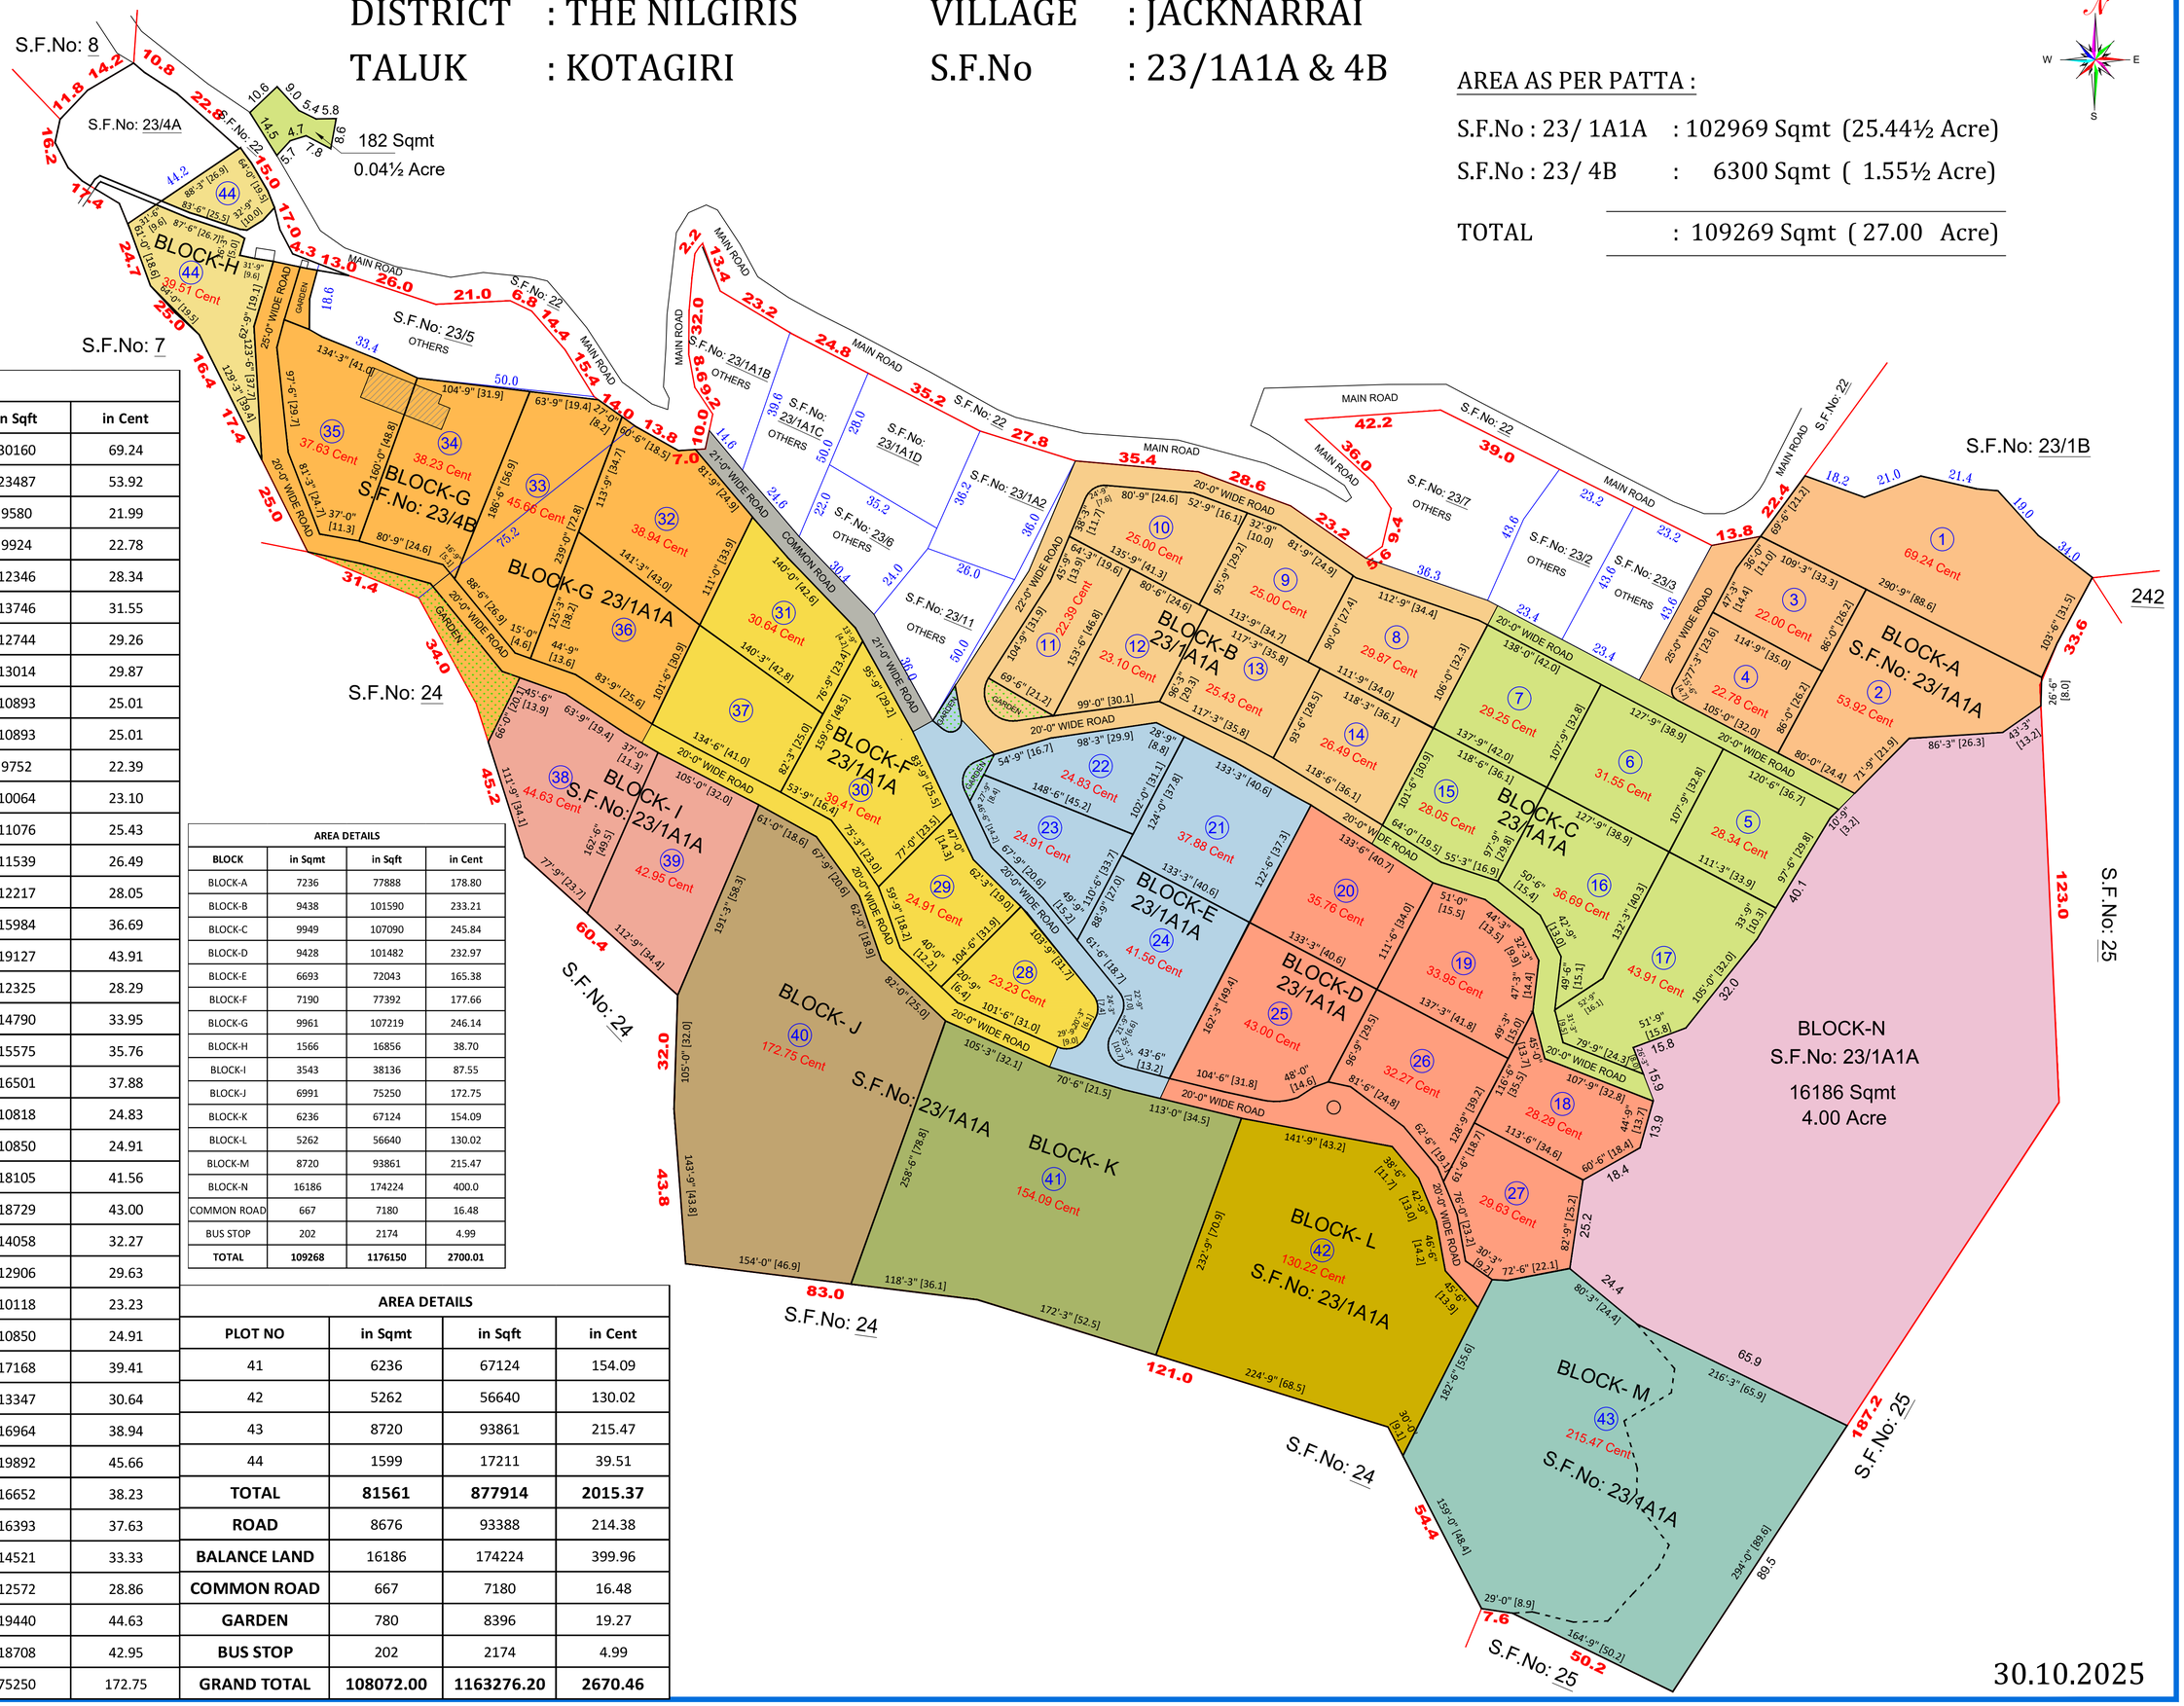

AREA DETAILS			
PLOT NO	in Sqmt	in Sqft	in Cent
1	2802	30160	69.24
2	2182	23487	53.92
3	890	9580	21.99
4	922	9924	22.78
5	1147	12346	28.34
6	1277	13746	31.55
7	1184	12744	29.26
8	1209	13014	29.87
9	1012	10893	25.01
10	1012	10893	25.01
11	906	9752	22.39
12	935	10064	23.10
13	1029	11076	25.43
14	1072	11539	26.49
15	1135	12217	28.05
16	1485	15984	36.69
17	1777	19127	43.91
18	1145	12325	28.29
19	1374	14790	33.95
20	1447	15575	35.76
21	1533	16501	37.88
22	1005	10818	24.83
23	1008	10850	24.91
24	1682	18105	41.56
25	1740	18729	43.00
26	1306	14058	32.27
27	1199	12906	29.63
28	940	10118	23.23
29	1008	10850	24.91
30	1595	17168	39.41
31	1240	13347	30.64
32	1576	16964	38.94
33	1848	19892	45.66
34	1547	16652	38.23
35	1523	16393	37.63
36	1349	14521	33.33
37	1168	12572	28.86
38	1806	19440	44.63
39	1738	18708	42.95
40	6991	75250	172.75

AREA DETAILS			
BLOCK	in Sqmt	in Sqft	in Cent
BLOCK-A	7236	77888	178.80
BLOCK-B	9438	101590	233.21
BLOCK-C	9949	107090	245.84
BLOCK-D	9428	101482	232.97
BLOCK-E	6693	72043	165.38
BLOCK-F	7190	77392	177.66
BLOCK-G	9961	107219	246.14
BLOCK-H	1566	16856	38.70
BLOCK-I	3543	38136	87.55
BLOCK-J	6991	75250	172.75
BLOCK-K	6236	67124	154.09
BLOCK-L	5262	56640	130.02
BLOCK-M	8720	93861	215.47
BLOCK-N	16186	174224	400.0
COMMON ROAD	667	7180	16.48
BUS STOP	202	2174	4.99
TOTAL	109268	1176150	2700.01

AREA DETAILS			
PLOT NO	in Sqmt	in Sqft	in Cent
41	6236	67124	154.09
42	5262	56640	130.02
43	8720	93861	215.47
44	1599	17211	39.51
TOTAL	81561	877914	2015.37
ROAD	8676	93388	214.38
BALANCE LAND	16186	174224	399.96
COMMON ROAD	667	7180	16.48
GARDEN	780	8396	19.27
BUS STOP	202	2174	4.99
GRAND TOTAL	108072.00	1163276.20	2670.46

30.10.2025